



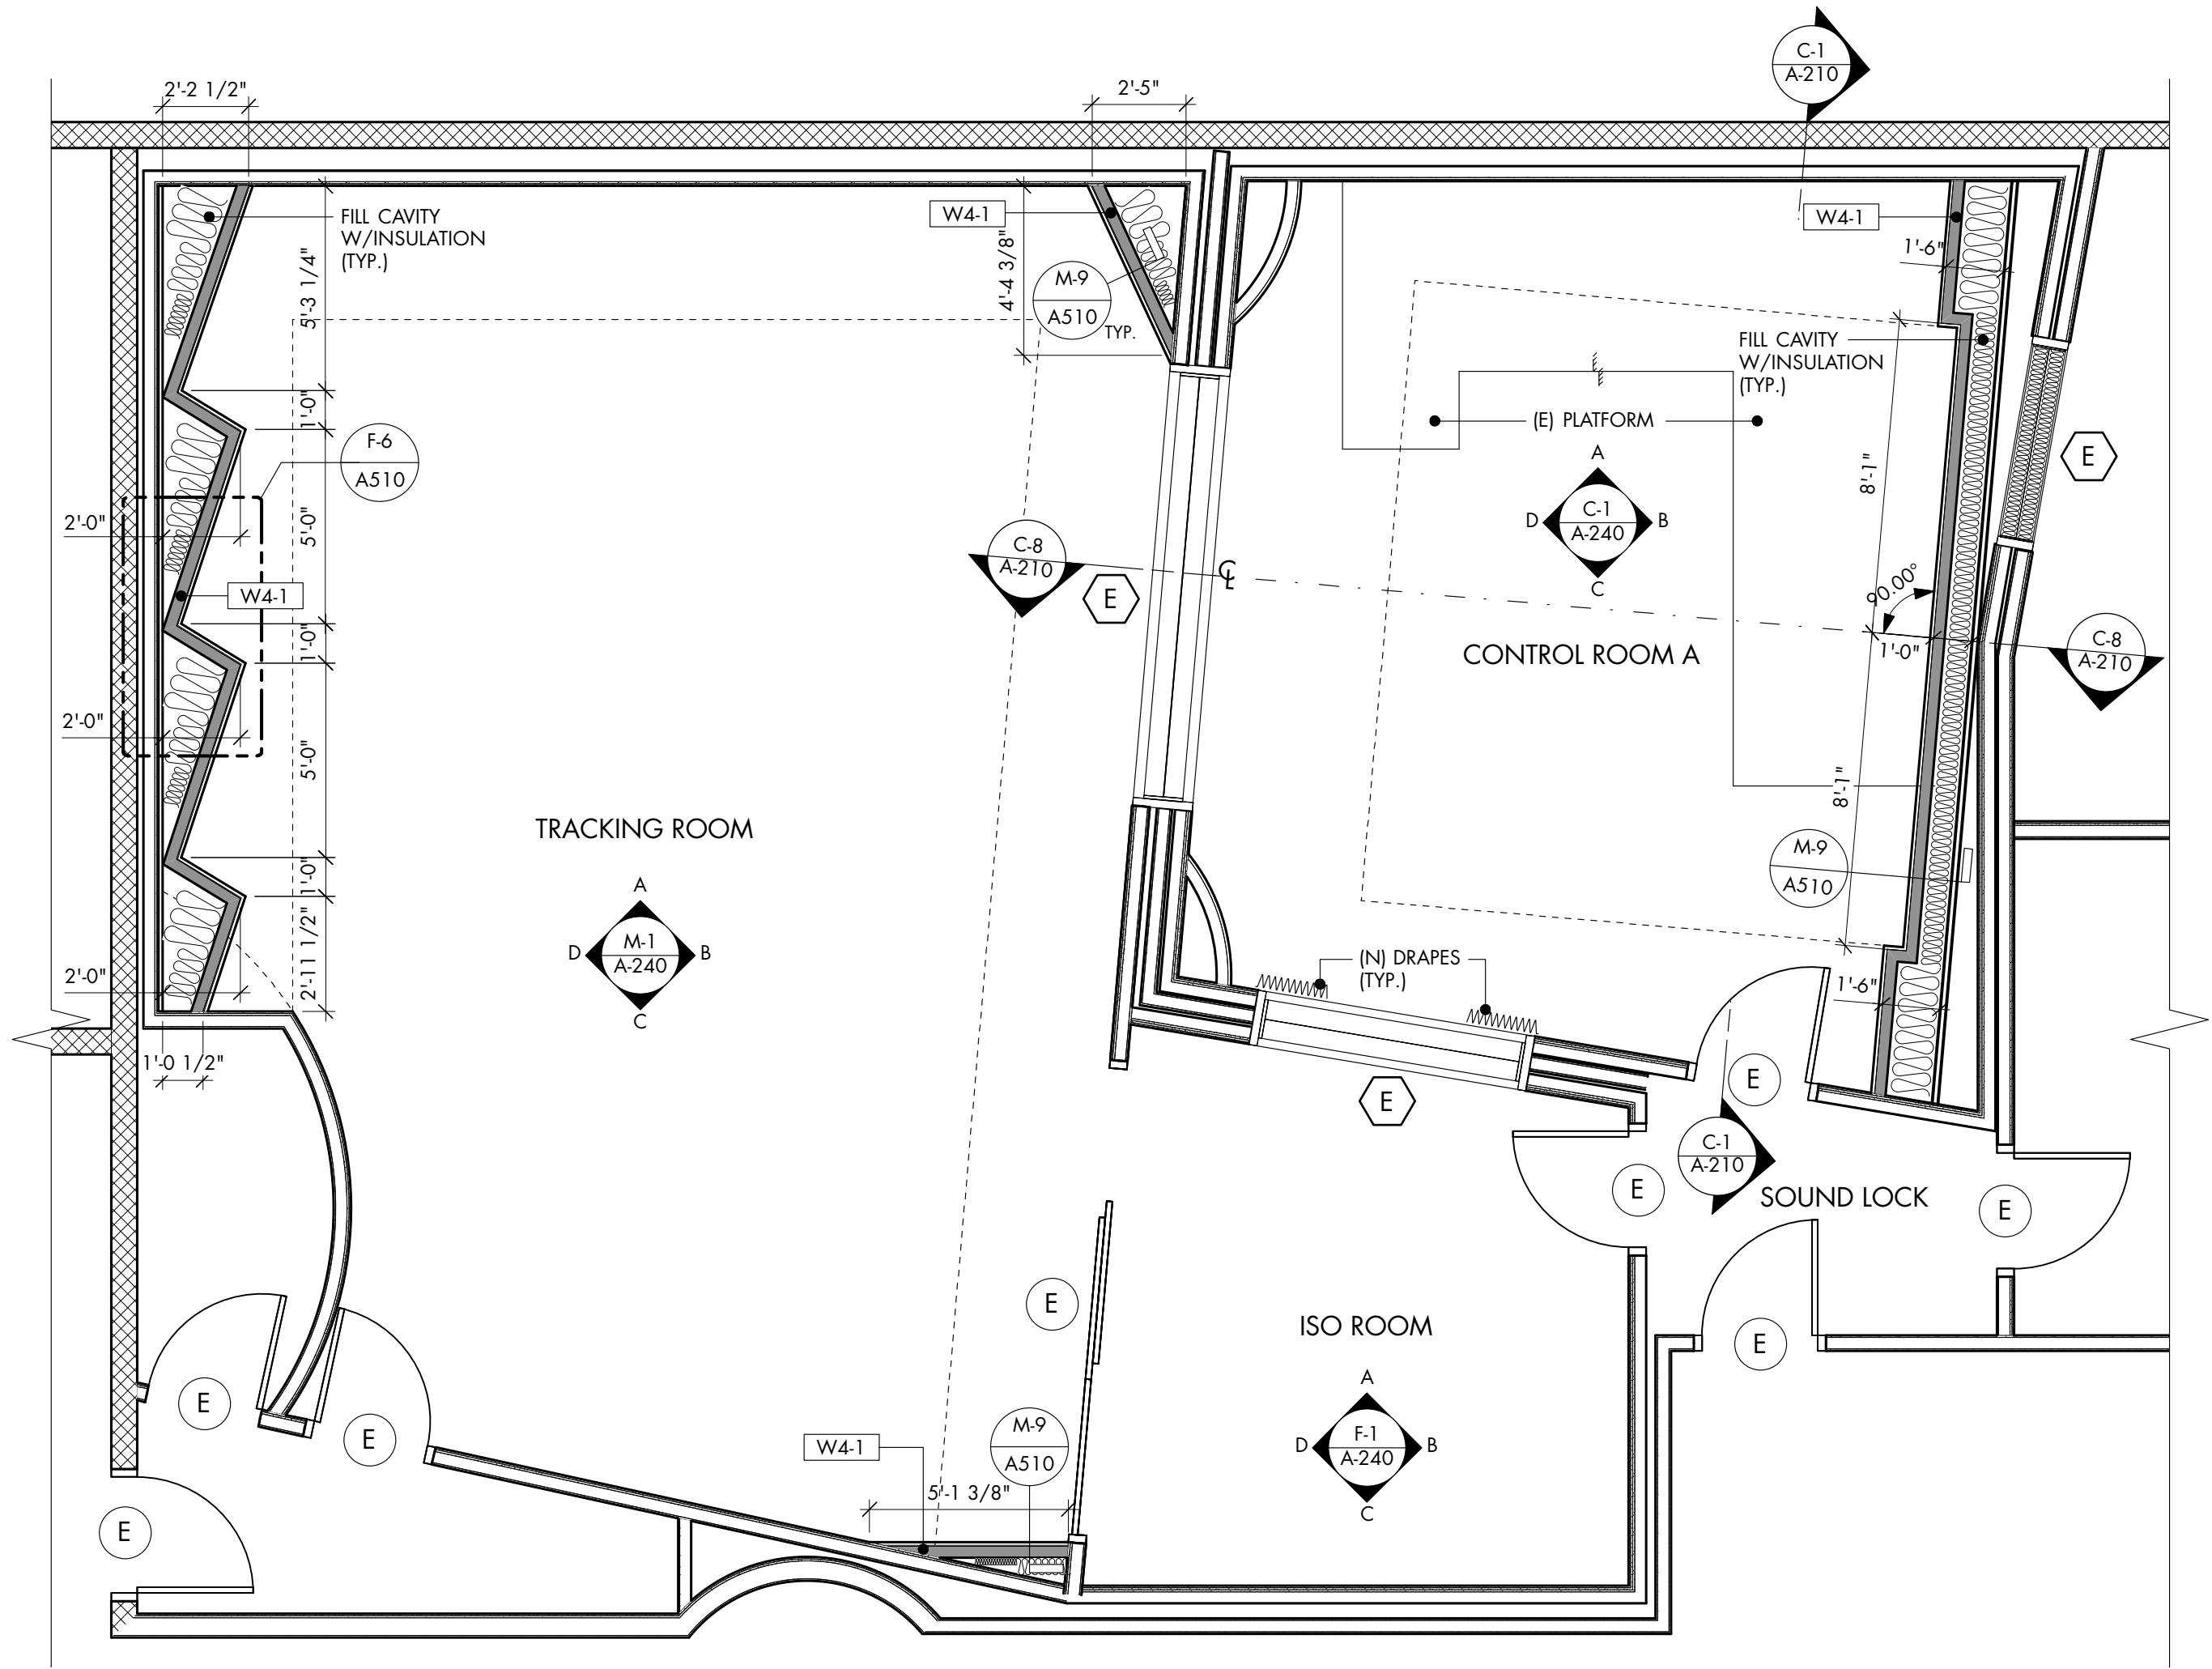

F-1 NEW CONSTRUCTION PLAN

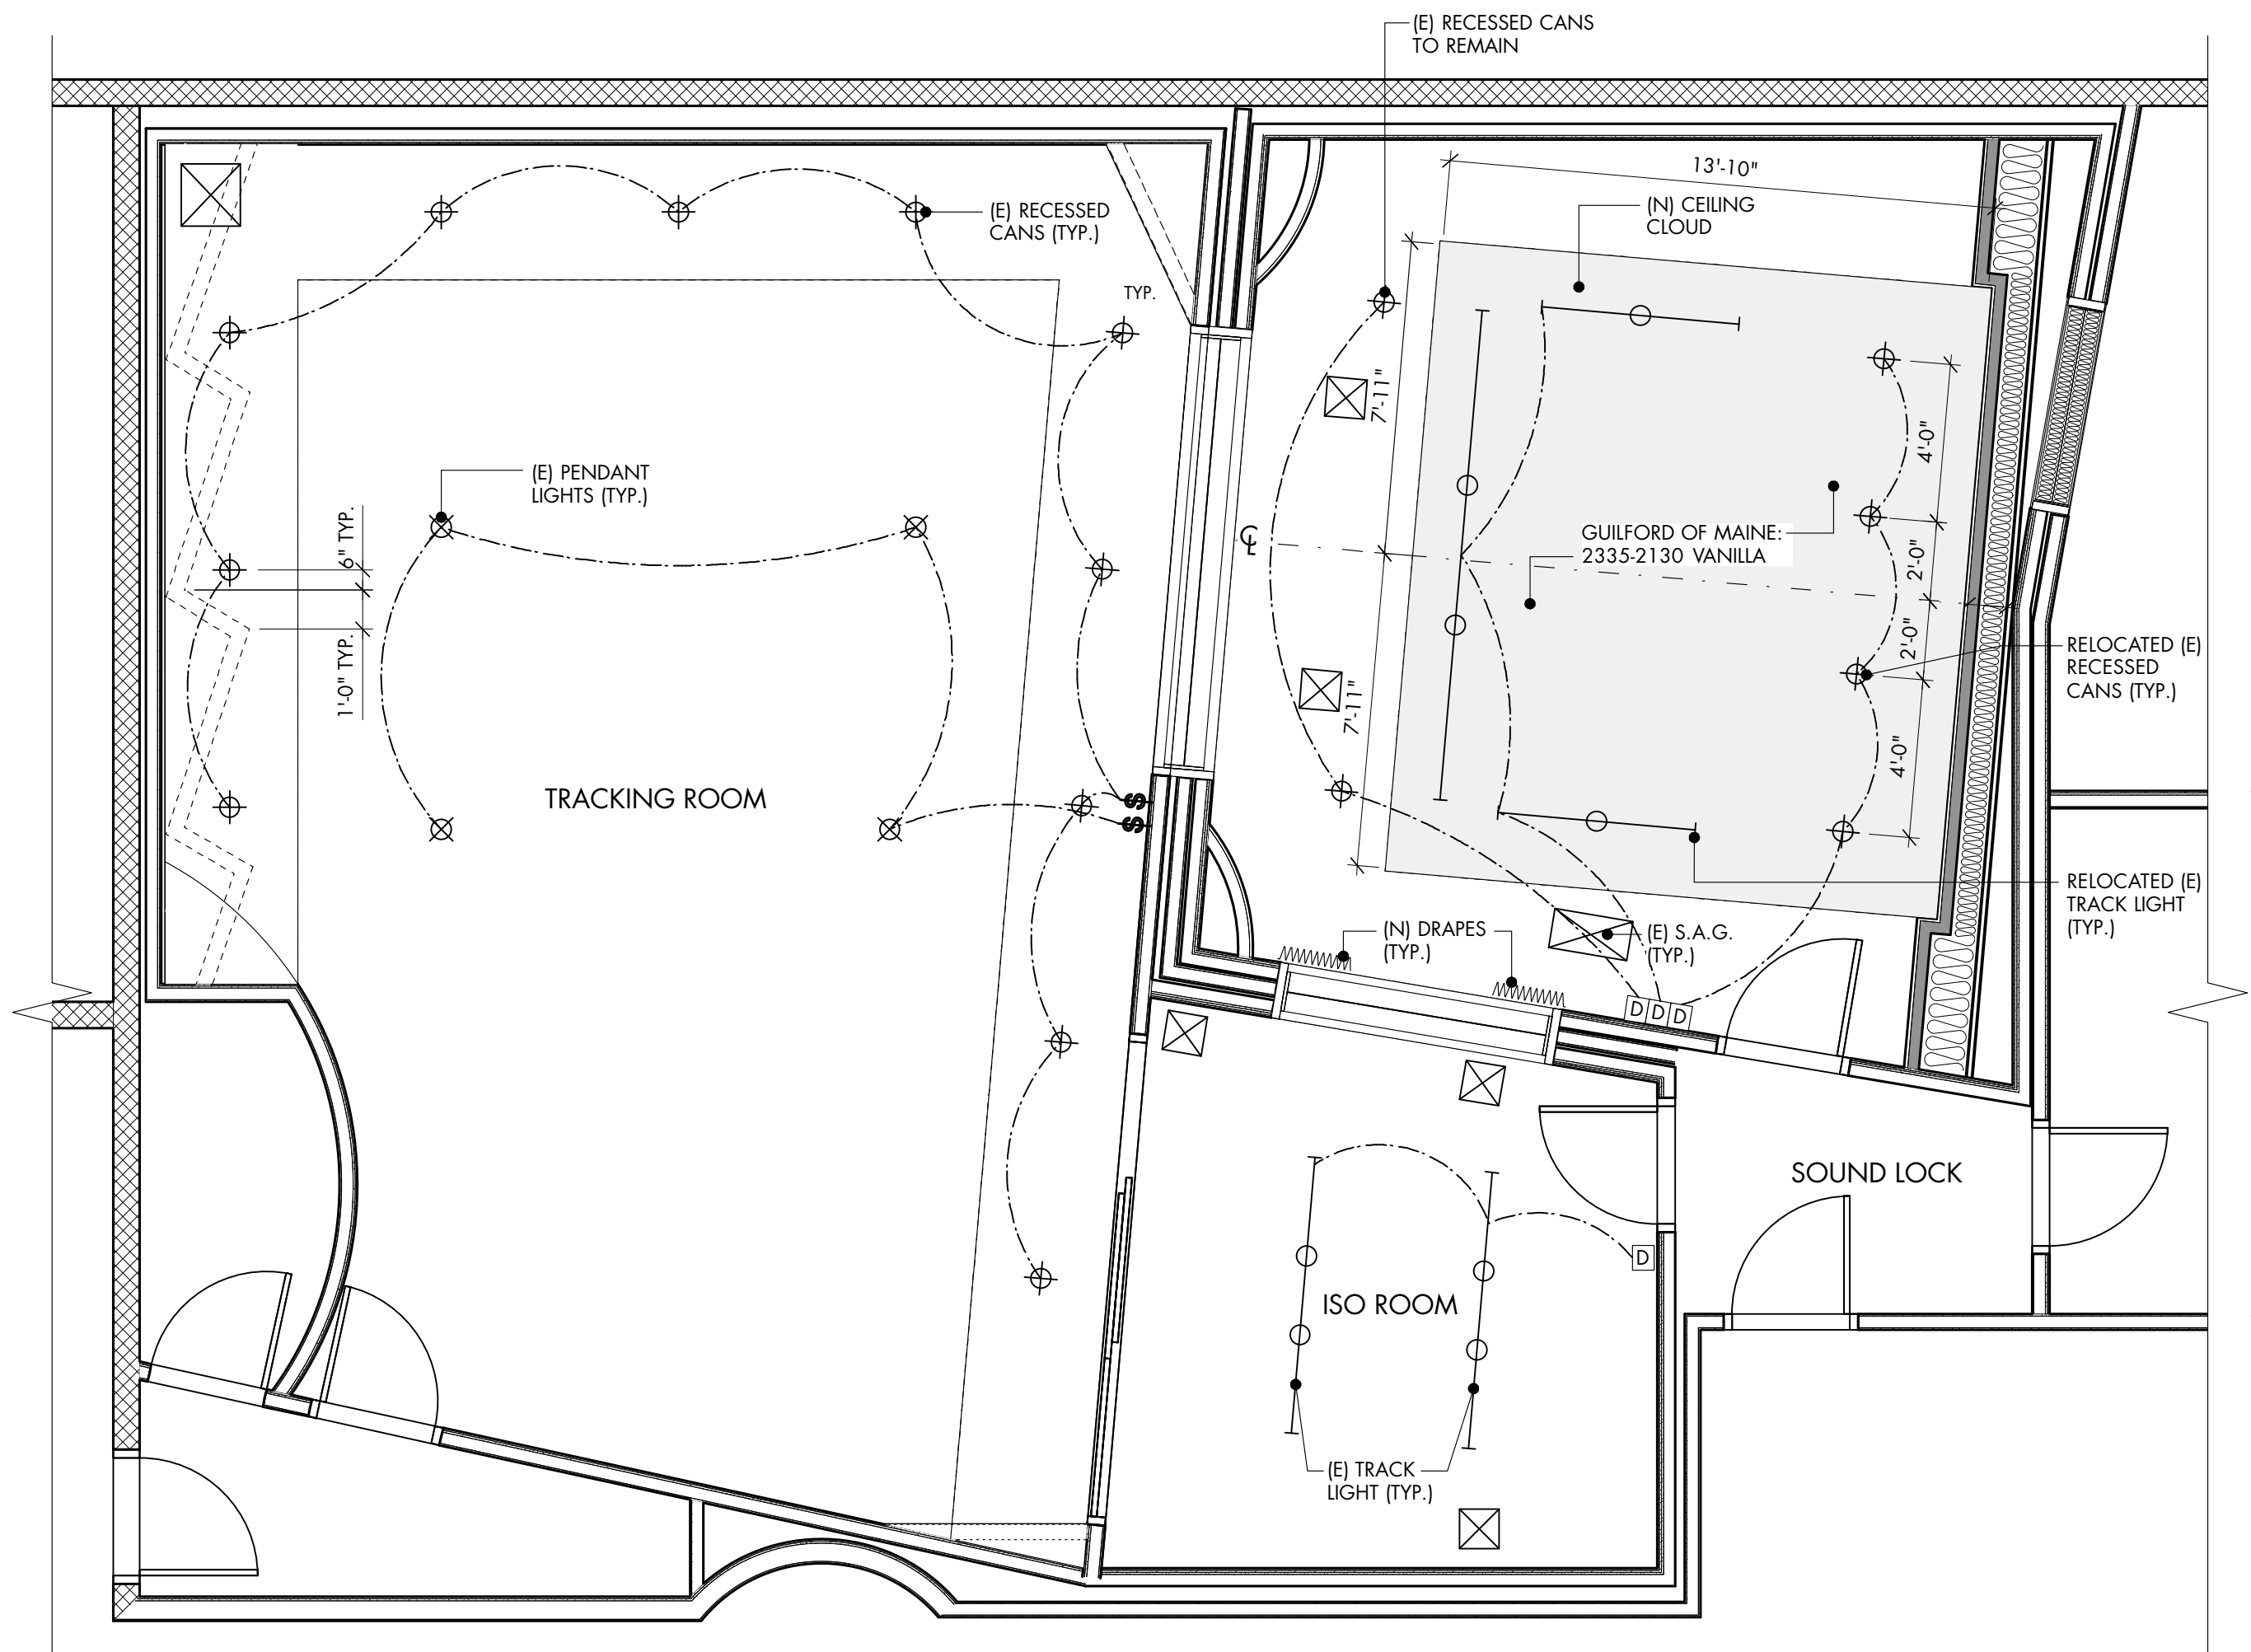

M-1 REFLECTED CEILING PLAN

THESE DOCUMENTS AND THEIR CONTENT CONTAIN INFORMATION PROPRIETARY TO nonzero\architecture AND ARE PROTECTED BY LEGAL COPYRIGHTS. ALL RIGHTS RESERVED. © nonzero\architecture

studio bauton
AUDIOVISUAL FACILITIES

PLAN LEGEND	
Room Name	Room Number
X	DOOR SYMBOL
X	WINDOW SYMBOL
1 A1	BUILDING SECTION
1 A1	DETAIL
A 1 A1 C	INTERIOR ELEVATION
●	DATUM, ELEVATION MARKER
X'XX" HD. HT.	DOOR, WINDOW HEAD HEIGHT
⌒	CENTER LINE
---	WALL TO REMOVE
(E) WALL	SEE WALL TYPES, A500
(N) WALL	SEE WALL TYPES, A500
F.G.	FINISH GRADE
F.F.	FINISH FLOOR
F.S.	FINISH SURFACE
F.H.	FULL HEIGHT WALL
T.P.	TOP PLATE
T.O.	TOP OF
B.O.	BOTTOM OF

NO.	DESCRIPTION	BY	DATE	NO.	DESCRIPTION	BY	DATE
1	CONSTRUCTION	DG	05.08.12				

KEYPLAN

nonzero\architecture
PETER GRUENEISEN FAIA

3200 AIRPORT AVENUE, SUITE 20
SANTA MONICA CALIFORNIA 90405


310 313 1000 telephone

info@nonzeroarch.com

www.nonzeroarch.com
www.bauton.com

TENANT IMPROVEMENT
STEVE JABLONSKY
PROJECT 1660 9TH ST., SANTA MONICA, CA 90404

NEW CONSTRUCTION/ REFLECTED
CEILING PLAN

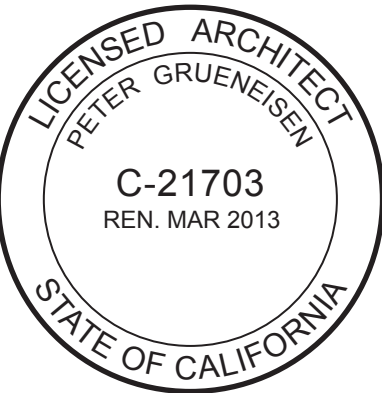

DATE	04.09.12	PROJECT NO.	28-306
DRAWN	MH/DG	A111	
REVIEWED	PG		
AS NOTED	SCALE		

STAMP
DATE: May 8, 2012
FILE NAME: CURRENT JABLONSKY AUDIOBANKS.vrx