



C-1 TRACKING ROOM

SCALE: 1/4" = 1'-0"

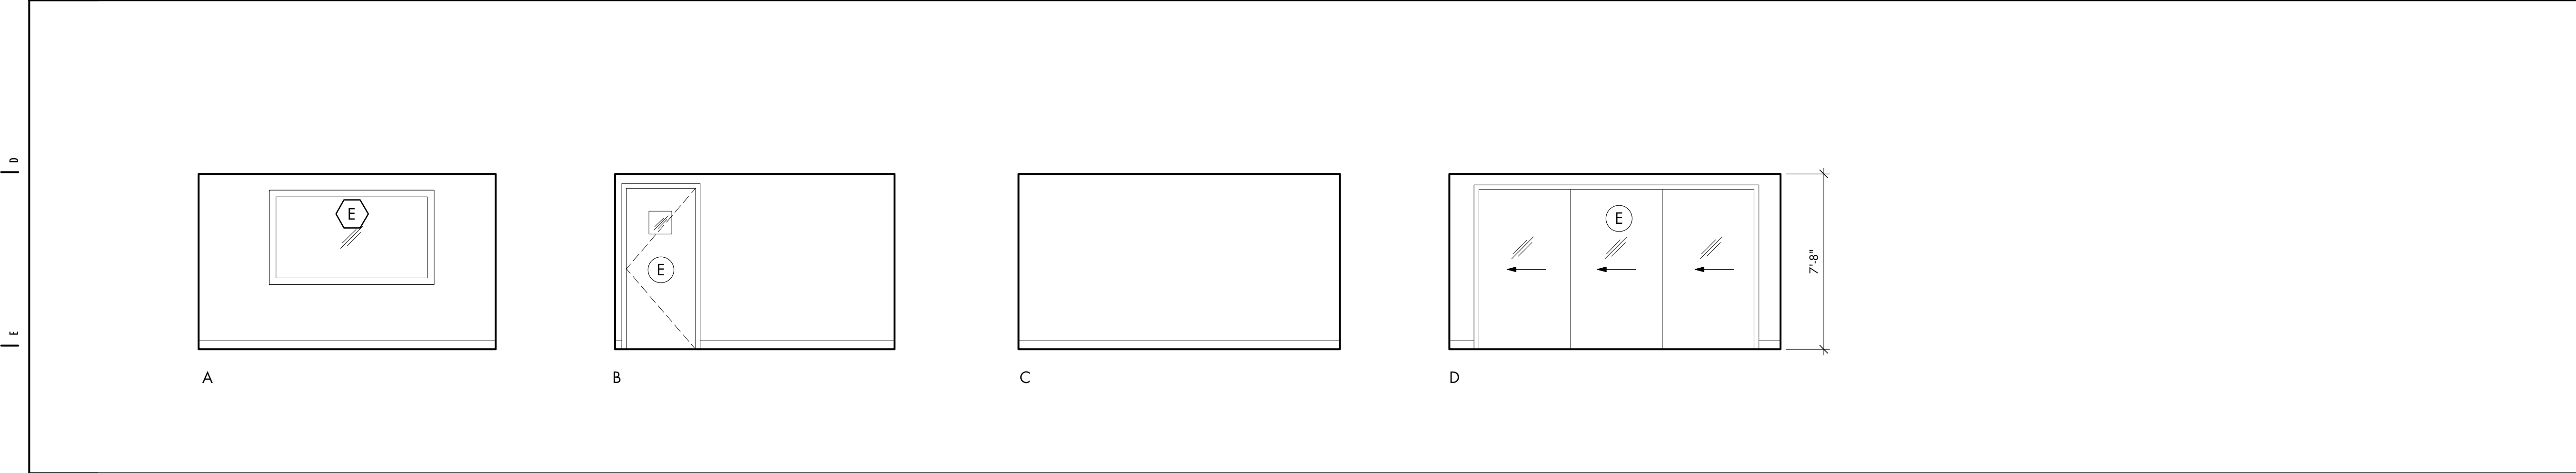

F-1 ISO ROOM

SCALE: 1/4" = 1'-0"

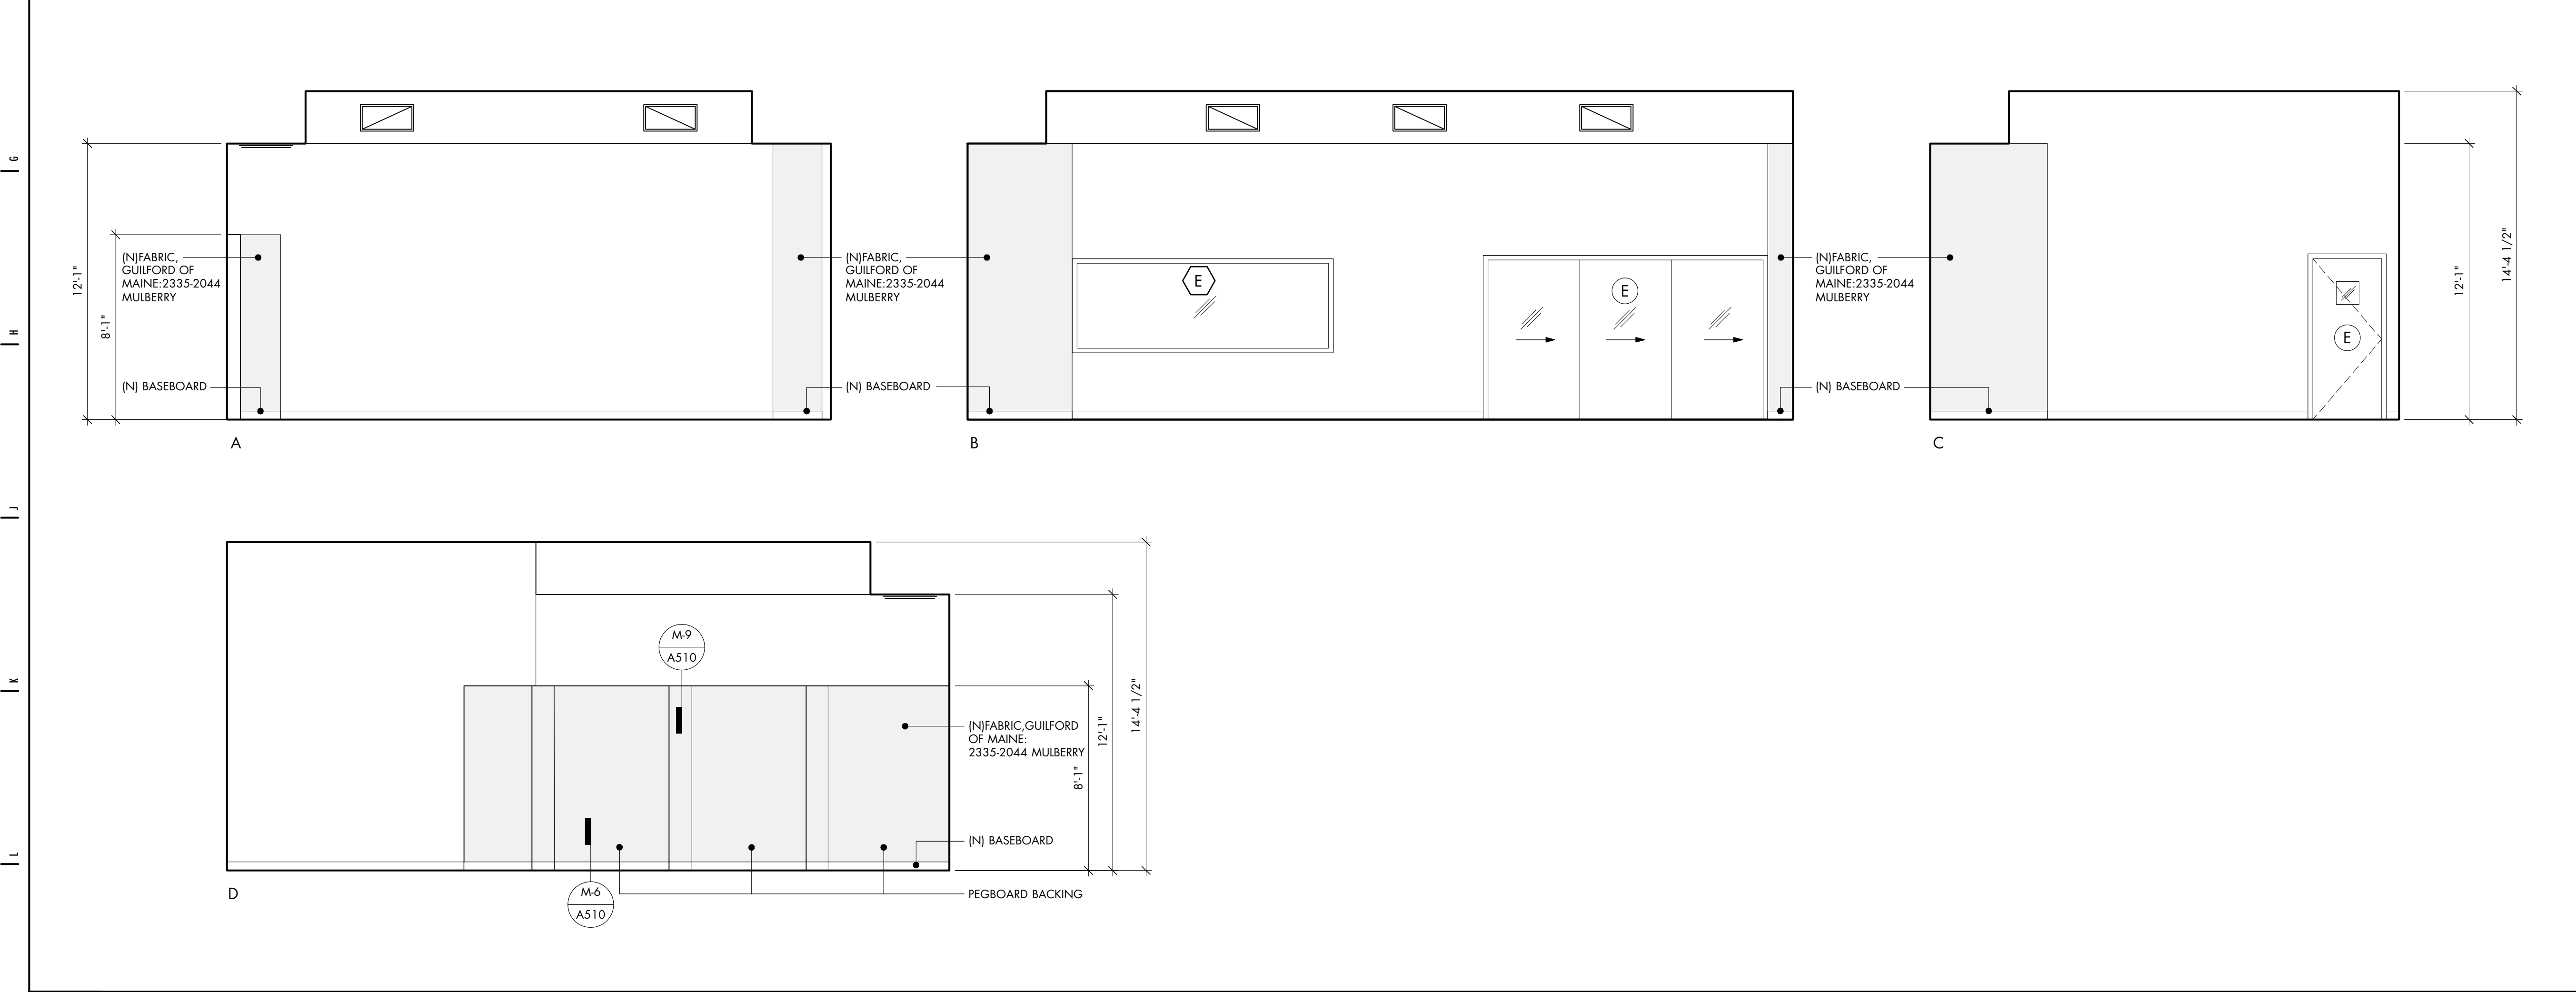

M-1 TRACING ROOM

SCALE: 1/4" = 1'-0"

THESE DOCUMENTS AND THEIR CONTENT CONTAIN INFORMATION PROPRIETARY TO
nonzero\architecture AND ARE PROTECTED BY LEGAL COPYRIGHTS.
ALL RIGHTS RESERVED. © nonzero\architecture

studio bauton
AUDIOVISUAL FACILITIES

PLAN LEGEND

Room Name
Room Number

X DOOR SYMBOL

X WINDOW SYMBOL

1 A1 BUILDING SECTION

1 A1 DETAIL

A 1 A1 B C INTERIOR ELEVATION

DATUM, ELEVATION MARKER

X:XX" HD. HT. DOOR, WINDOW HEAD HEIGHT

C CENTER LINE

WALL TO REMOVE

(E) WALL - SEE WALL TYPES, A500

(N) WALL - SEE WALL TYPES, A500

F.G. FINISH GRADE
F.F. FINISH FLOOR
F.S. FINISH SURFACE
F.H. FULL HEIGHT WALL
T.P. TOP PLATE
T.O. TOP OF
B.O. BOTTOM OF

NO	DESCRIPTION	BY	DATE	NO.	DESCRIPTION	BY	DATE
1	CONSTRUCTION	DG	05.08.12				

KEYPLAN

nonzero\architecture
PETER GRUENEISEN FAIA

3200 AIRPORT AVENUE, SUITE 20
SANTA MONICA CALIFORNIA 90405

310 313 1000 telephone
info@nonzeroarch.com
www.nonzeroarch.com
www.bauton.com

TENANT IMPROVEMENT
STEVE JABLONSKY
PROJECT 1660 9TH ST., SANTA MONICA, CA 90404

INTERIOR ELEVATIONS

DRAWING	DATE	PROJECT NO.
04.09.12	28-306	
MH/DG		
DRAWN		
PG		
REVIEWED		
AS NOTED		
SCALE		

A240

DRAWING NO.

Stamp: LICENSED ARCHITECT PETER GRUENEISEN C-21703 REN. MAR 2013 STATE OF CALIFORNIA

Stamp: MAY 8, 2012

File name: CURRENT JABLONSKY AUDIOBANKS.vrx