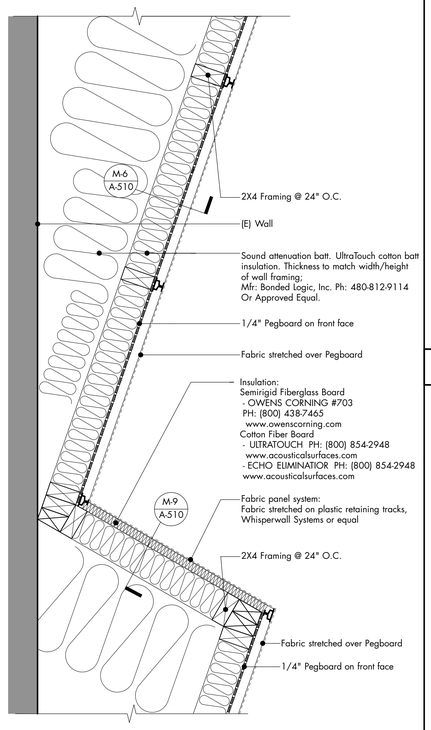

F-6 DETAIL SCALE: 1 1/2" = 1'-0"

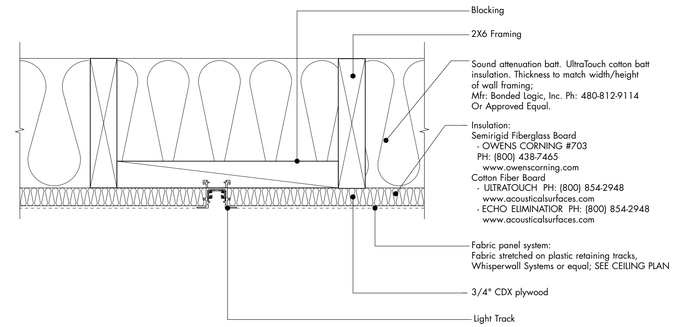

C-9 DETAIL @ LIGHTING TRACK SCALE: 3" = 1'-0"

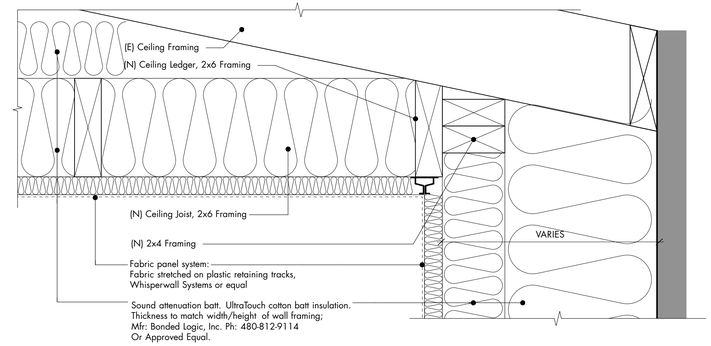

F-9 DETAIL @ CEILING CLOUD

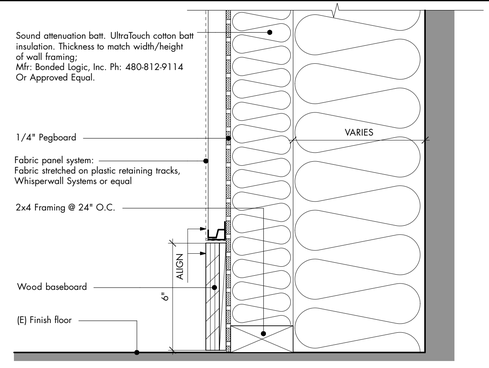

J-9 DETAIL @ BASE SCALE: 3" = 1'-0"

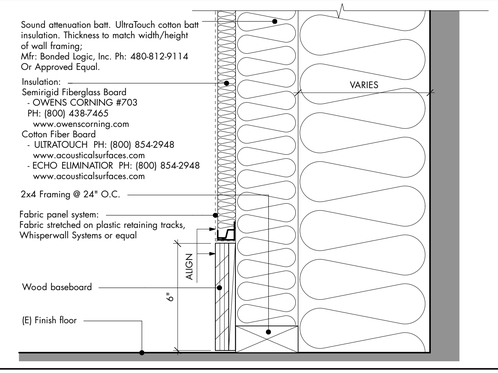

M-9 DETAIL @ BASE SCALE: 3" = 1'-0"

THESE DOCUMENTS AND THEIR CONTENT CONTAIN INFORMATION PROPRIETARY TO nonzero\architecture AND ARE PROTECTED BY LEGAL COPYRIGHTS.
ALL RIGHTS RESERVED. © nonzero\architecture

studio **bau:ton**
AUDIOVISUAL FACILITIES

- EXISTING CONSTRUCTION
- INSULATION
- SOLID WOOD
- PLYWOOD
- MDF
- GYPSUM BOARD
- STUCCO
- GROUT / CEMENT BOARD
- CONCRETE
- PRECAST CONCRETE
- CONCRETE MASONRY UNIT
- STONE
- BRICK
- STEEL
- ALUMINUM
- GLASS
- RUBBER
- EARTH
- SAND
- GRAVEL

NO	DESCRIPTION	BY	DATE	NO.	DESCRIPTION	BY	DATE
1	CONSTRUCTION	DG	05.08.12				

KEYPLAN

nonzero\architecture
PETER GRUENEISEN FAIA

3200 AIRPORT AVENUE, SUITE 20
SANTA MONICA CALIFORNIA 90405

310 313 1000 telephone

info@nonzeroarch.com

www.nonzeroarch.com
www.bauton.com

PROJECT
TENANT IMPROVEMENT
STEVE JABLONSKY
1660 9TH ST., SANTA MONICA, CA 90404

DRAWING
CONSTRUCTION & FINISH DETAILS

STAMP
LICENSED ARCHITECT
PETER GRUENEISEN
C-21703
REN. MAR 2013
STATE OF CALIFORNIA

DATE 04.09.12
DRAWN MH/DG
REVIEWED PG
SCALE AS NOTED

PROJECT NO. **28-306**

DRAWING NO. A510

Date: May 8, 2012
File name: CURRENT JABLONSKY AUDIOBANKS.vwx